


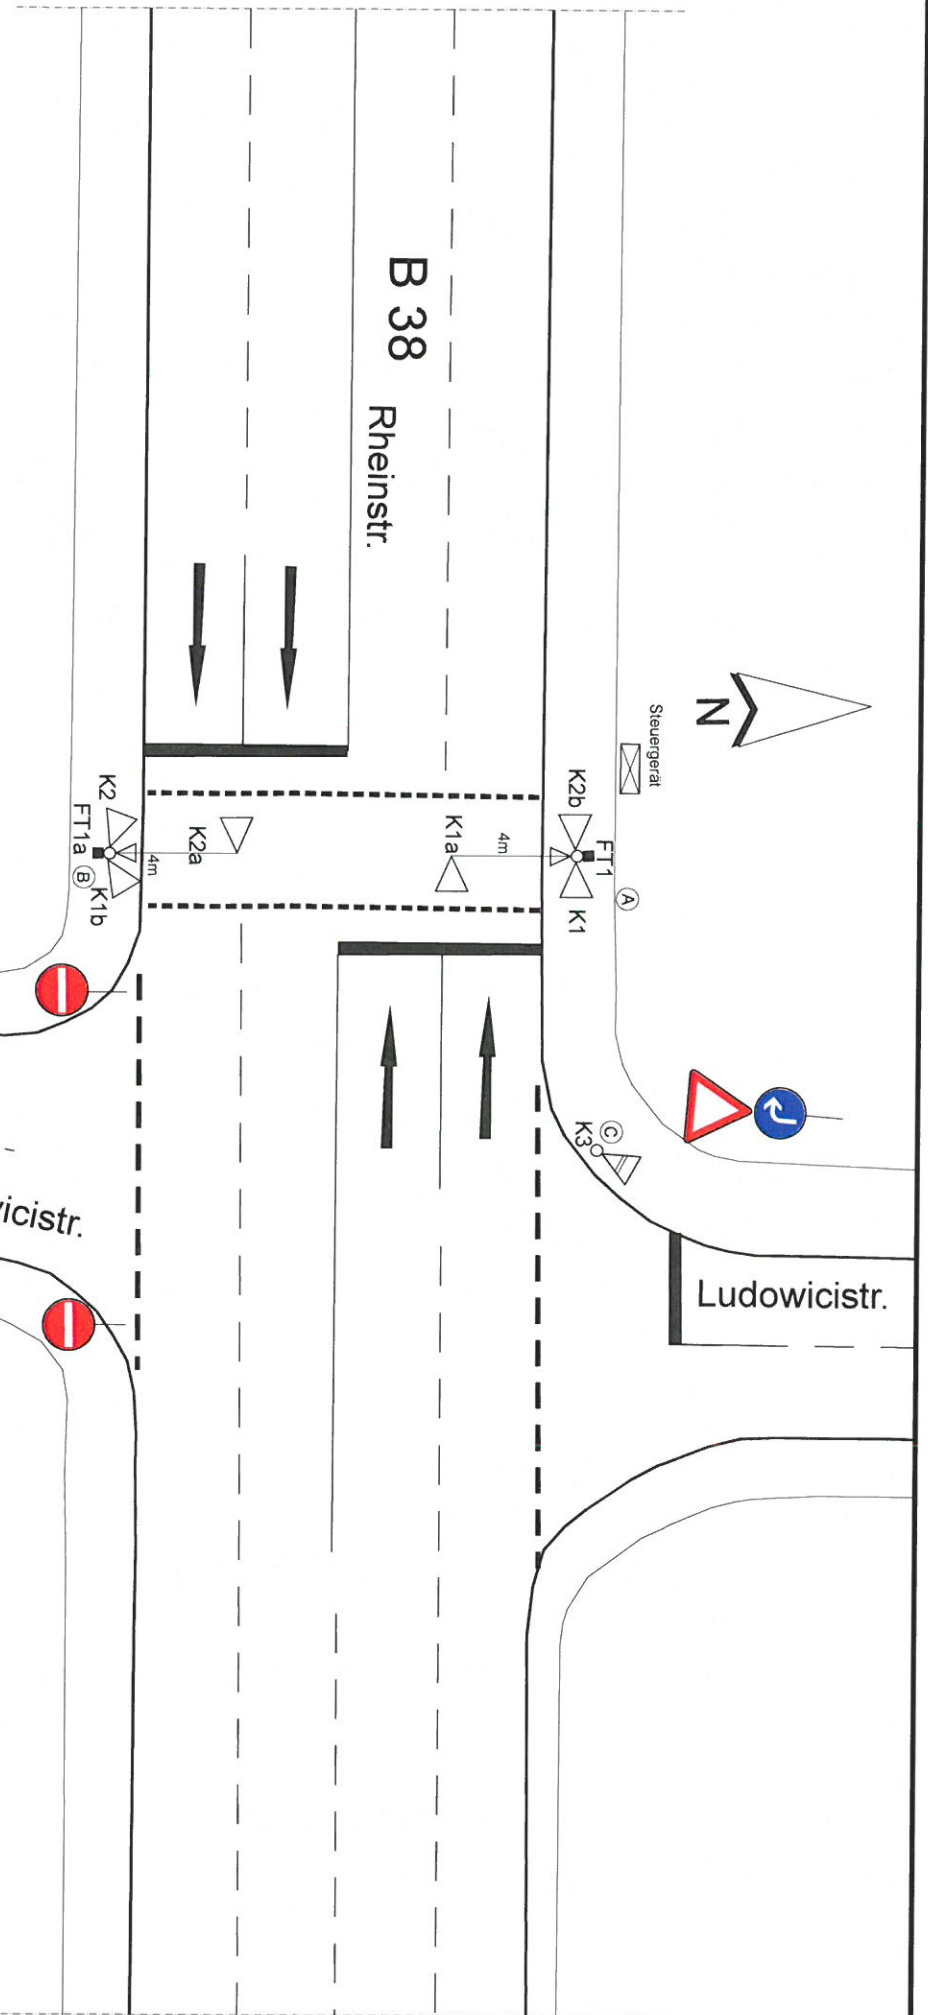

SIGNALGRUPPEN	K1, K1a, K1b K2, K2a, K2b	F1, F1a	K3
Ø	200	Ø	200
ROT	Ø	Ø	Ø
GELB	Ø	Ø	Ø
GRÜN	Ø	Ø	Ø

Schutzvermerk nach DIN 34 beachten				Art
ZVA	Datum	Name	DAMBACH-WERKE GmbH Verkehrssystemsyste Postfach 1160 - 76449 Kuppenheim Tel.: 07222 / 402-0 Fax 07222 / 402-200	Blatt 1
Bearbeitet	17.10.08	Oehme		Amt Stadt Landau
Gezeichnet	17.10.08	Lust		Abt. Straße
Geprüft				Anlage-Nr.
Maßstab	Benennung	LSA B 38 Rheinstr. / Ludowicistr. in LANDAU, alz		ES 08-372
1:500				

