
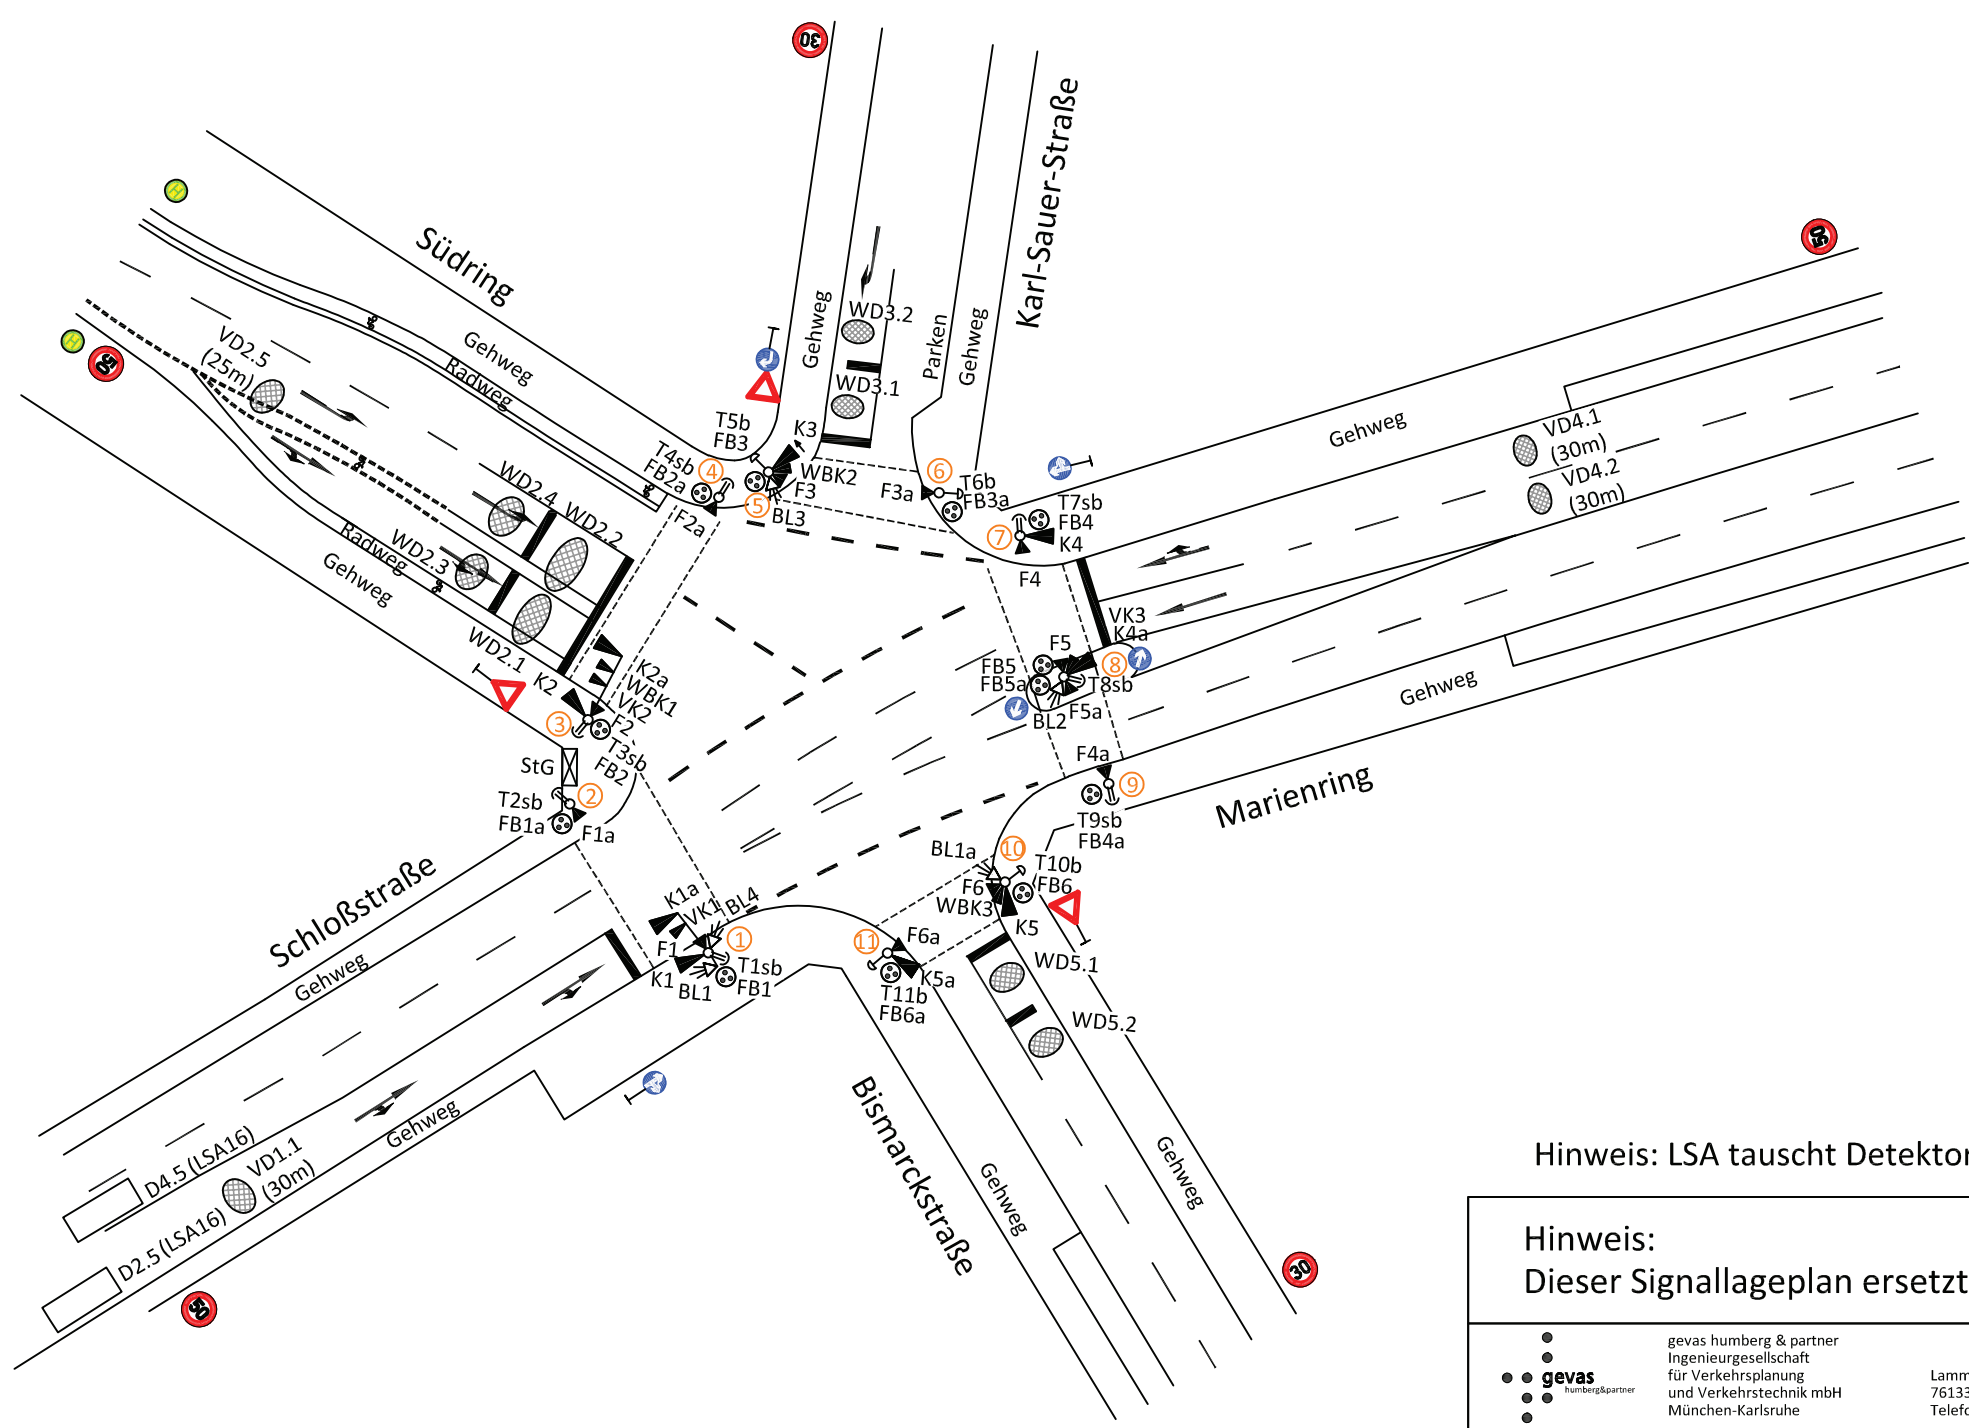


- Legende:
- Dx = Induktionsschleife
 - VDx = Videofeld
 - WDx = Wärmefeld (Video)
 - Tx_b = Druckkontakt Blinde
 - Tx_sb = Druckkontakt Sehende und Blinde
 - Kx = Kfz-Signalgeber
 - Kx = Kfz-Signalgeber mit Blende
 - Rx = Rad-Signalgeber
 - Fx = Fußgänger-Signalgeber
 - ⊕ = Blindenausstattung
 - VKx = Videokamera
 - WBKx = Wärmebildkamera (Video)
 - ① = Mastnummer
 - StG = Steuergerät

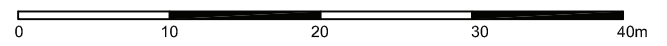

Hinweis: LSA tauscht Detektordaten mit LSA 16 aus (Planung)

Hinweis:
Dieser Signallageplan ersetzt nicht den Beschilderungs- und Markierungsplan !

gevas humberg&partner
Ingenieurgesellschaft
für Verkehrsplanung
und Verkehrstechnik mbH
München-Karlsruhe

Lammstraße 21
76133 Karlsruhe
Telefon 0721 / 831 835 - 0

Signallageplan

Signal- gruppen	K1, K2, K4, K5			K3									BL1 BL3	BL1a BL2 BL4	F1, F2, F3, F4, F5, F6	
Ø	200			200									200	300	200	
ROT	○	↶	↷	↷	↶	↷	⬮	⬮					⤴	⤴	⤴	⤴
GELB	○	↶	↷	↷	↶	↷	⬮	⬮					⤴	⤴	⤴	⤴
GRÜN	○	↶	↷	↷	↶	↷	⬮	⬮					⤴	⤴	⤴	⤴

Nr.	Änderung	Zeichen	Plan-Nr.	1/1	Stadt: Stadt Landau Knoten: LSA 10 Marienring/ Südring/ Bismarckstraße
			Datum	17.04.2020	
			Bearbeiter	ba / esk	
			Maßstab	1 : 500	
S:\LD_Landau_LSA\LSA 10\LSA10_1\Zeichenbüro\LD_LSA10					