


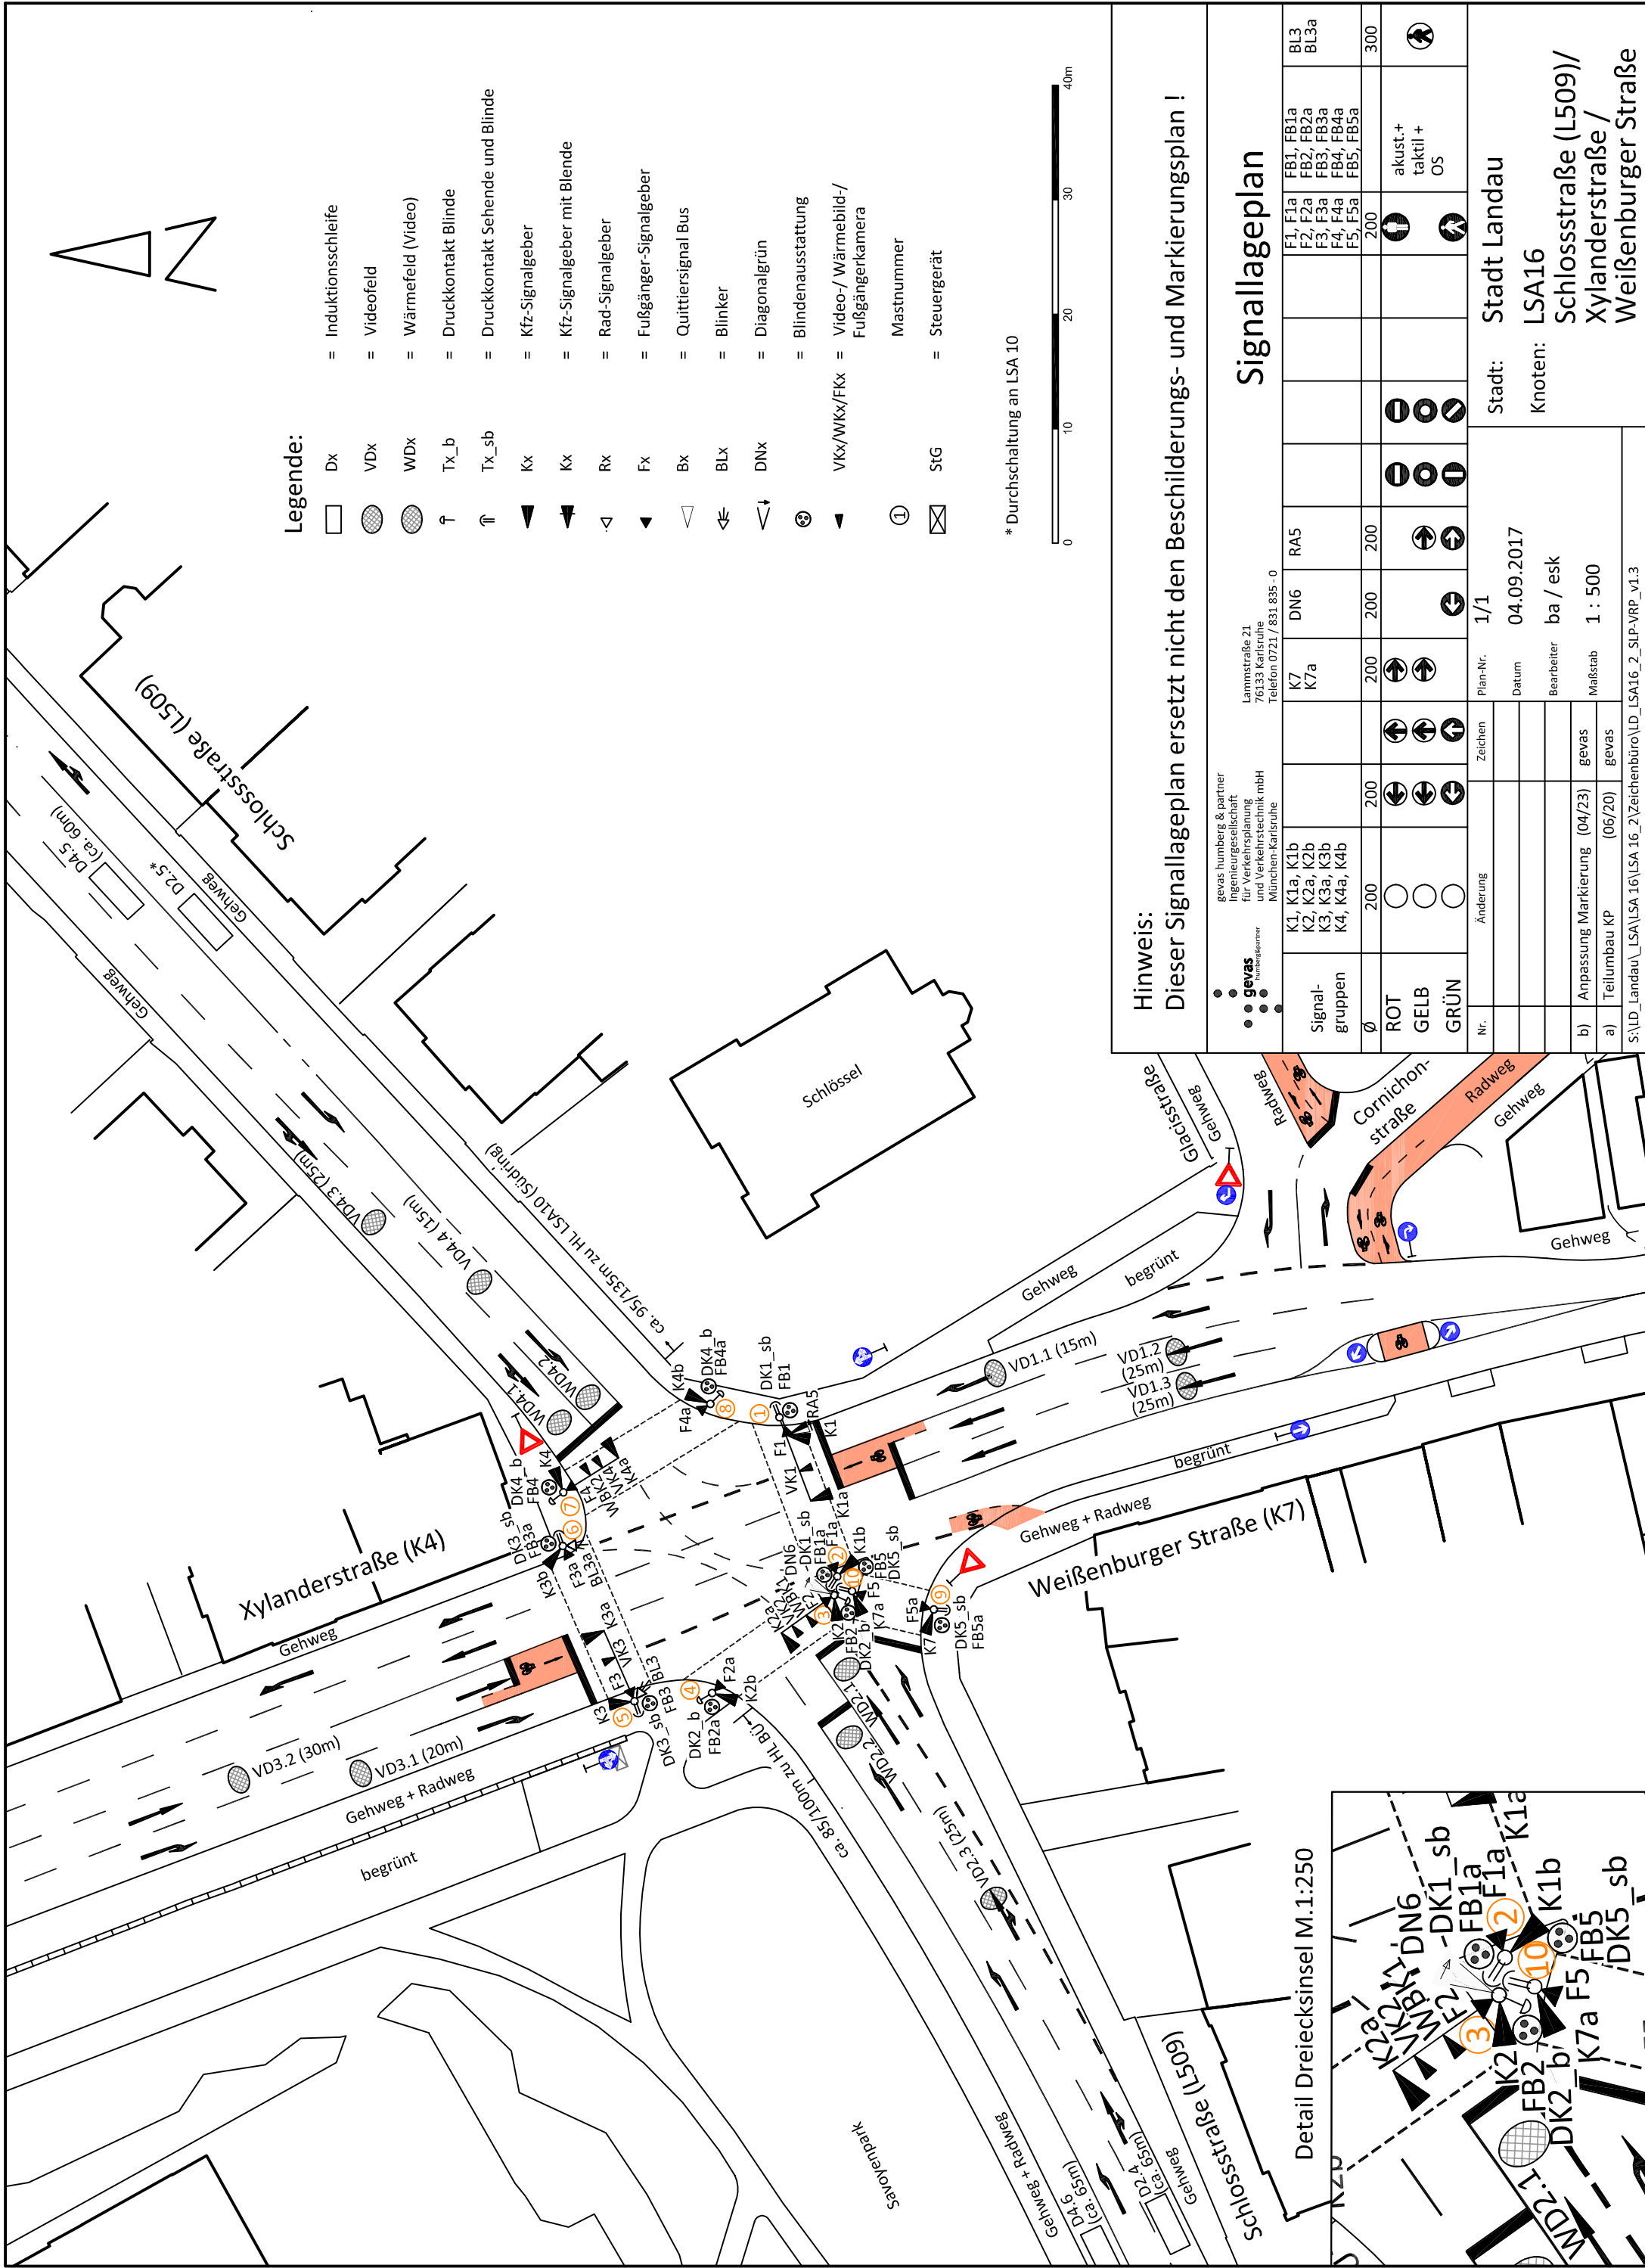

gevas humb&partner gevas humberg & partner Ingenieurgesellschaft für Verkehrsplanung und Verkehrstechnik mbH München-Karlsruhe Lammstraße 21 76133 Karlsruhe Telefon 0721 / 831 835 - 0 Signallageplan											
Signalgruppen	K1, K1a, K1b K2, K2a, K2b K3, K3a, K3b K4, K4a, K4b	200	200		K7 K7a	DN6	RA5		F1, F1a F2, F2a F3, F3a F4, F4a F5, F5a	FB1, FB1a FB2, FB2a FB3, FB3a FB4, FB4a FB5, FB5a	BL3 BL3a
Ø		200	200		200	200	200		200		300
ROT	○	↔	↔	↕	↕			⊖	⬆	akust.+ taktill + OS	♿
GELB	○	↔	↔	↕	↕		↗	⊖			
GRÜN	○	↔	↔	↕	↕	↖	↘	↗	♿		
Nr.	Änderung	Plan-Nr.		1/1		Stadt Landau					
		Datum		04.09.2017		Knoten: LSA16					
		Bearbeiter		ba / esk		Schlossstraße (L509) // Xyländerstraße / Weißenburger Straße					
b)	Anpassung Markierung (04/23)	gevas		Maßstab							
a)	Teilumbau KP (06/20)	gevas									