


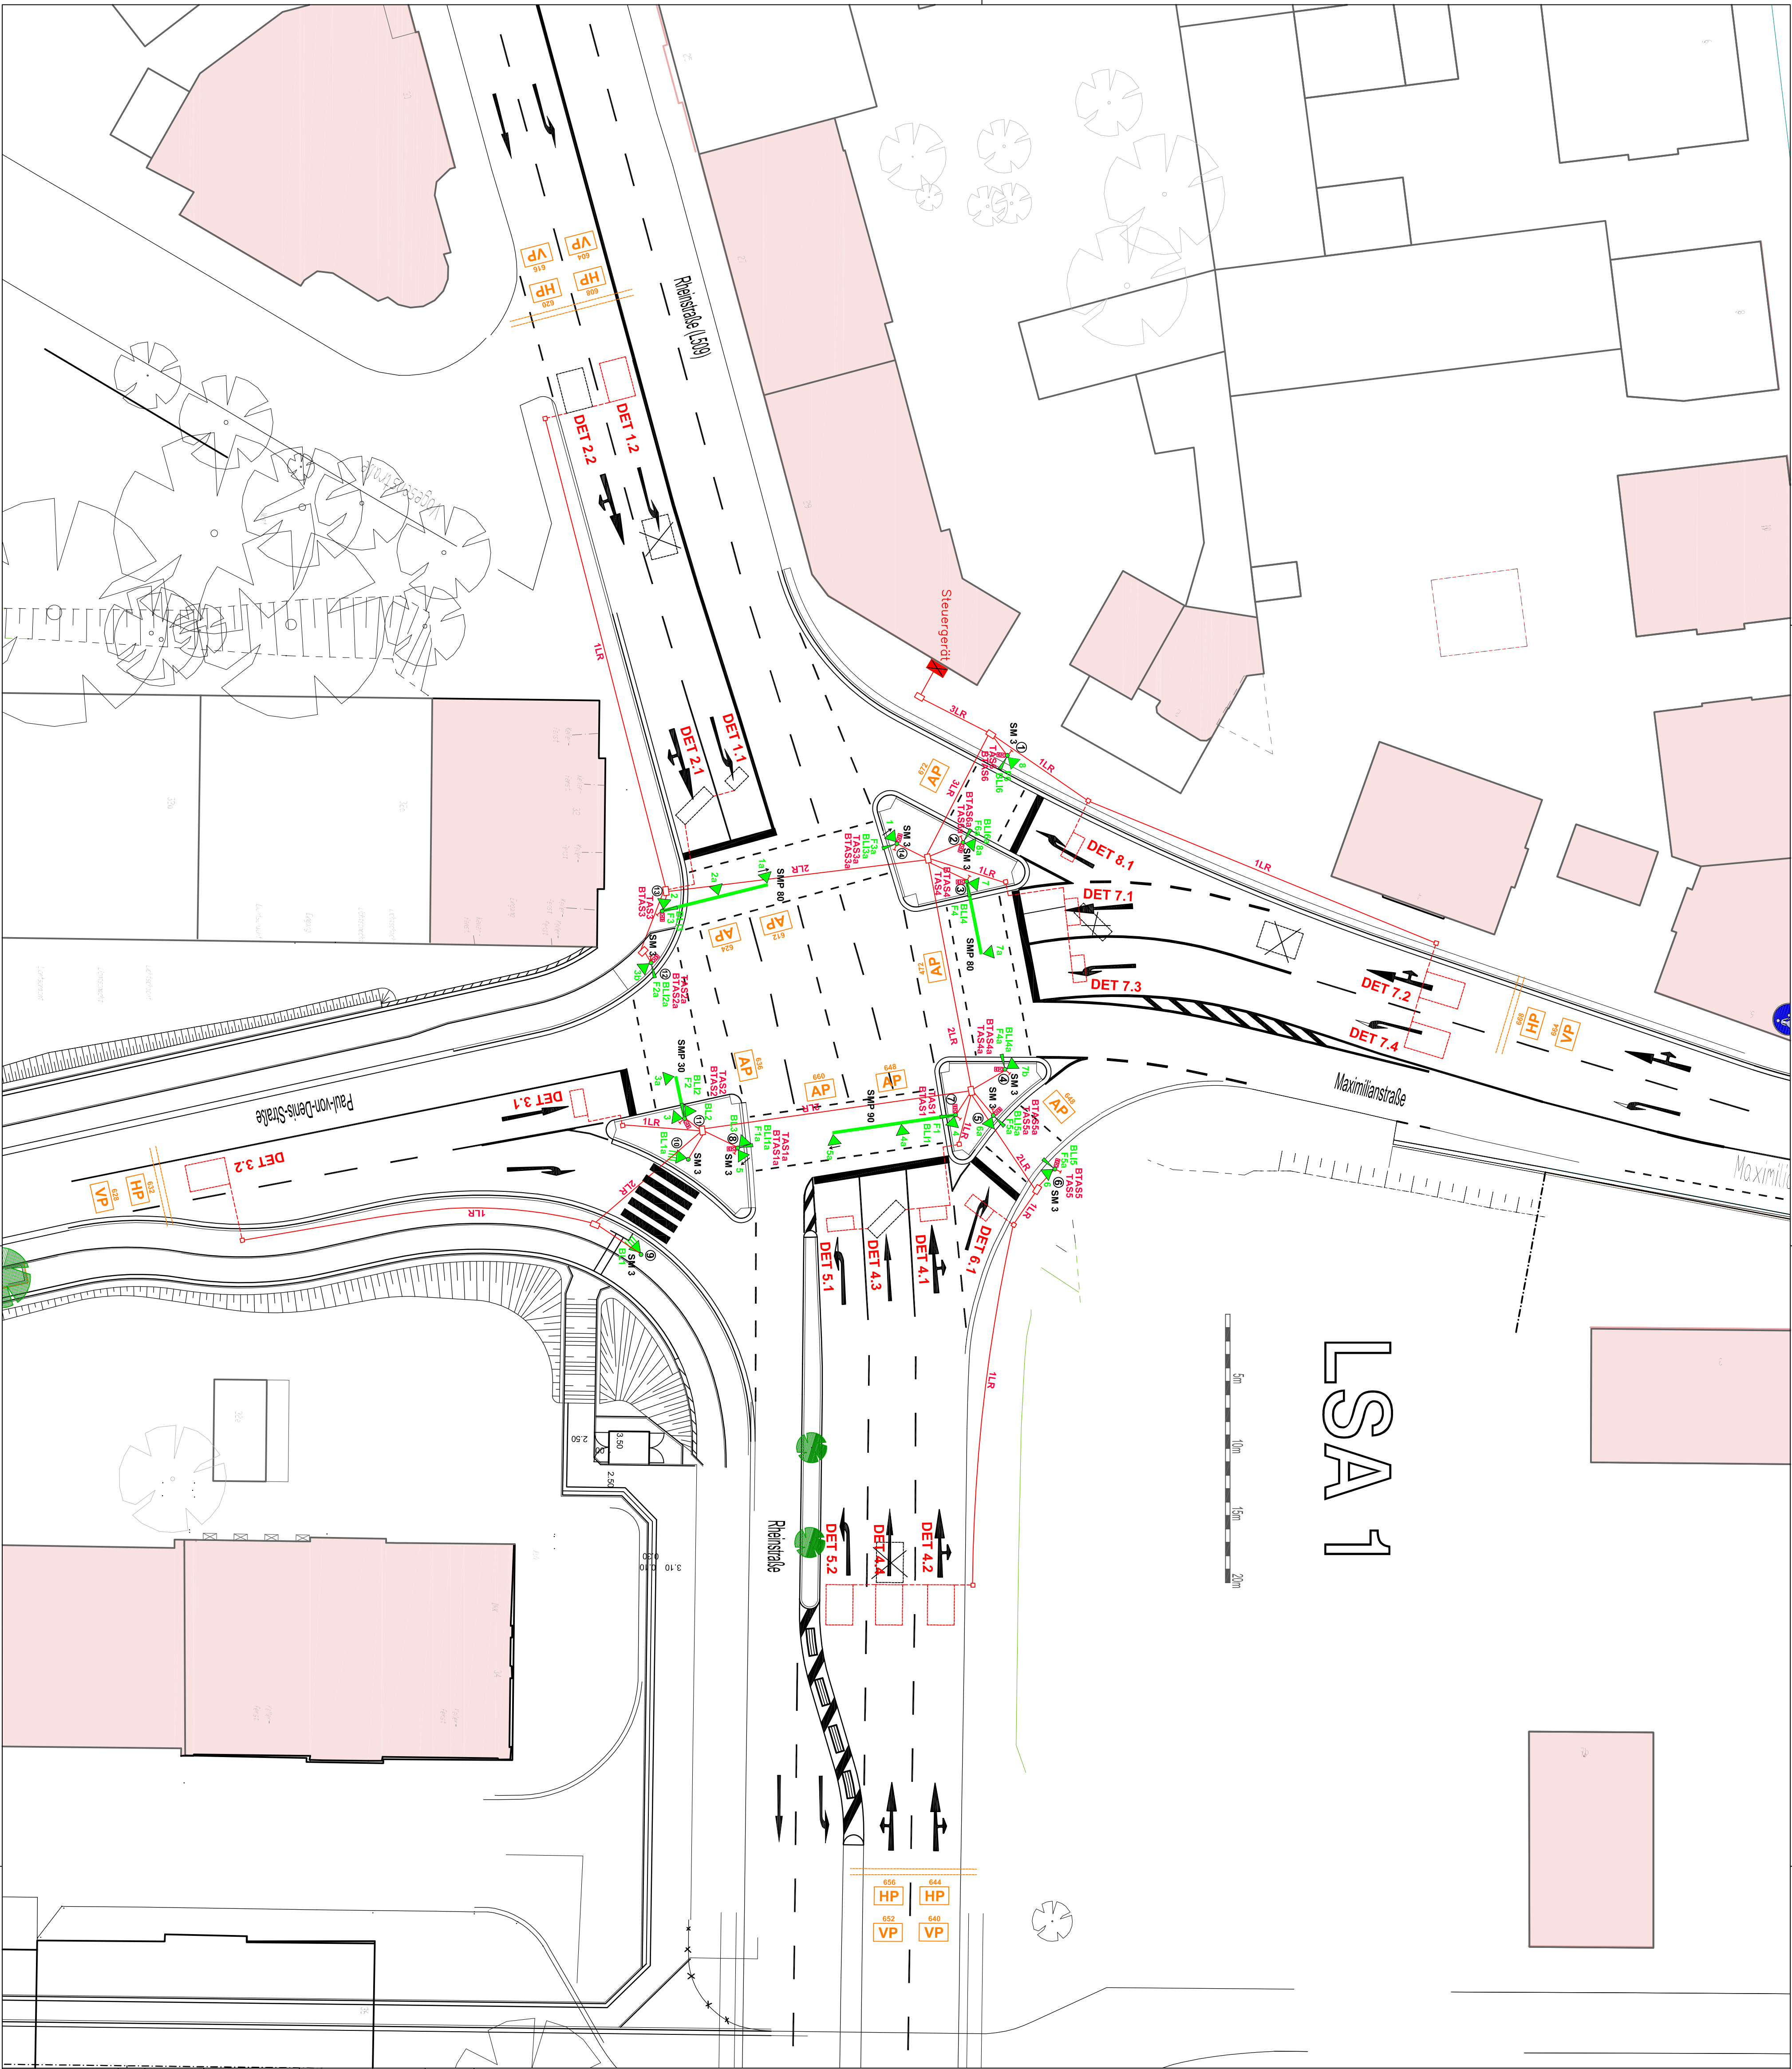

LSA 1

5m 10m 15m 20m

①	Signalgruppen-Nr.
▽	Signalgeber Bestand
▲	Signalgeber Planung
●	Signalmast mit Ausleger Planung
—	Kabelverlegung
—	Kabelverlegung in vorh. Leerrohr
—	vorh. Steuerkabel VSR
—	Induktionsschleife Bestand
—	Induktionsschleife Planung
—	Blindenraster Planung
—	Fußgängeraster Planung
—	Fußgängeraster Bestand
—	Steuergerät Planung
—	Steuergerät Bestand
—	Hauptanmeldung
—	Voranmeldung
—	Abmeldung
—	Video camera
—	Video camera-Messfeld
②	Mastnummer
③	Signalrohrmast L = 3m ü. Gel.
④	SM mit Ausleger L = 6 m
⑤	Anzahl Leerrohre

Die Sichtfelder im Kreuzungsbereich müssen freigehalten werden.

AUSFÜHRUNGSPLANUNG

STADT LANDAU IN DER PFALZ

LSA 1
LS09 RHEINSTRASSE /
MAXIMILIANSTRASSE

SIGNALTECHNISCHE PLANUNG
DER LSA 1

Signallageplan M. 1:250

Stand 07/13

JOACHIM SCHWAB
PLANUNGSBÜRO FÜR
STRASSEN- UND
TRASSEN-ENTWURF
DEUTL. SAARBRÜCKEN
TEL: 0681 / 9071-700-500