


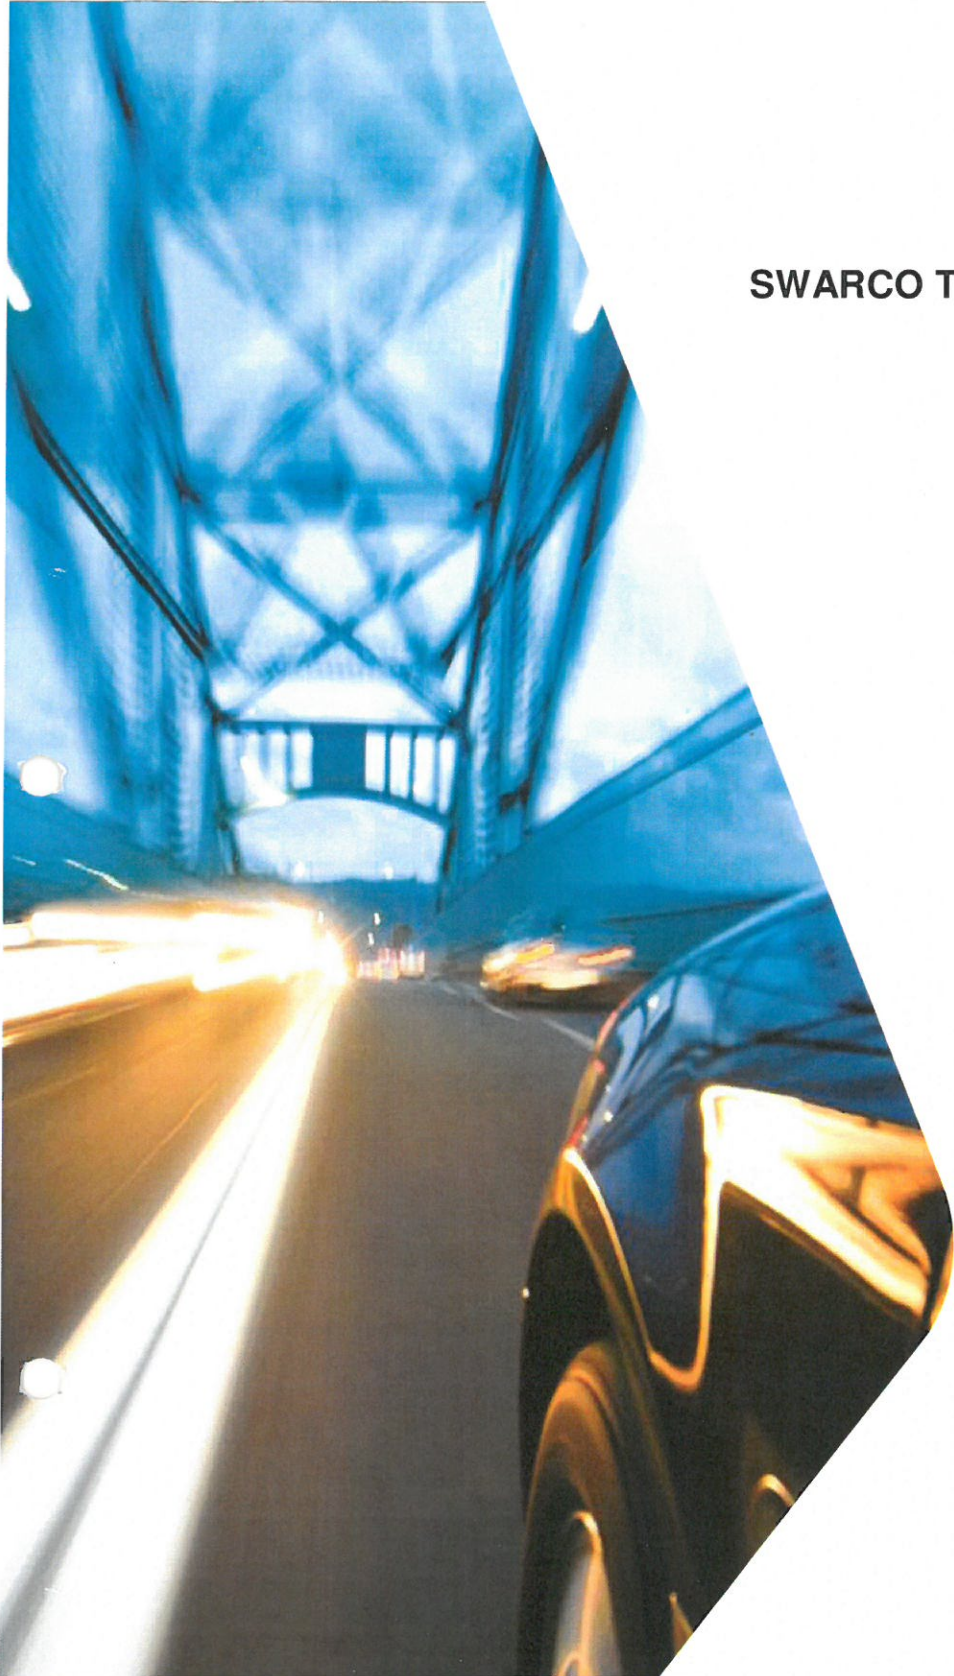

SWARCO TRAFFIC SYSTEMS GMBH

A photograph of a bridge at night, viewed from below. The bridge's steel structure is illuminated with blue light. In the foreground, a car is visible, its headlights and taillights creating bright orange and yellow light trails. The background shows other vehicles and the bridge's arches receding into the distance.

Steuergeräteversorgung M844

LSA Landau L509/ Marienring-Ostring-Moltkestraße.
EQ 2009875 ES92_998b

Juli 2013

SWARCO | First in Traffic Solutions.

Auftrag	856940075961	Auftragsart	C09K	M-Tech Berechenbare Vertragsleistun
Beschreibung	Programmänderung K3 Grünzeit, H. Schillin			
Starttermin	25.06.2013	Endtermin	25.06.2013	
Priorität				
Status	FREI ABRV KKMP VOKL			
Techn.Platz	VT1-VRS1-186567	Stadt Landau		
Equipment	2009875	L 509 / Marienring-Ostring-Moltkestraße		
STG-Typ				
Tech.Ident-Nr.	LANDAU			
Baugruppe				
Standort				
IH-Planergruppe	718	Gaggenau Nord STP	Raum	
V.Arbeitsplatz	S1-TD-GN	C207	IH-Werk	C207
Wartungsplan	GN-Gaggenau Nord-TD-VRS			
RevisionNr	Wart.planPos			

Auftraggeber 186567 Telefon 06341/13-471

Adresse
Stadt Landau
Stadtbauamt Abt. 660/S3
Königstraße
D- LANDAU IN DER PFALZ

Auftragskoordinator 93 Telefon 07022/6025-146

Adresse
Rist
SWARCO TRAFFIC SYSTEMS GMBH
Niederlassung Unterensingen
Kelterstraße
D- UNTERENSINGEN

Klasse	EQ1	Vertriebs- und Technikmerkmale	002
LAMPENSPANNUNG		230V LED	
VERTRAGSART		Wartungsvertrag	
Klasse	EQ2	VT_Merkmale	002
VT_ABTEILUNG		VR-Süd	
Vorgang	0010	Programmänderung K3 Grünzeit, H. Schillin	
Status	FREI		
Arbeitsplatz	S1-TD-GN	C207	GN-Gaggenau Nord-TD-VRS
Steuerschlüssel	VT01		Rückmeldenummer 1493738
Vorgangsschl.			Meilenstein
Techn.Platz			
Equipment			
STG-Typ	M-8XX (Dambach)		
Arbeit	0,0 STD	Leistungsart	SHTDP
Dauer	0,0 STD	Anzahl	0
Früh.Startdatum	25.06.2013	Startuhrzeit	07:00:00
Spät.Enddatum	25.06.2013	Enduhrzeit	07:00:00
Istarbeit	0,0 STD	Gesamtpuffer	0 STD

Ende des Berichts

Schillinger Stefan (STS)

Von: Manz Arno (STS)
Gesendet: Donnerstag, 20. Juni 2013 12:59
An: Schillinger Stefan (STS)
Betreff: Landau ES 92_998
Anlagen: Landau20.06-13.txt

92/998a

Hallo Stefan

Beider Anlage Landau B38 Marienring am Gericht ES 92_998 soll die Grünzeit des K3 um 5 Sekunden verlängert werden.

Im Programm 3 und Programm 4.

Mit freundlichen Grüßen

Arno

2009 875

Besonderheiten

Keine

Serielle Anschlüsse

Zentrale	DVI35	X
	OCIT	
	SB15	
	SSI	
	Telis	
	VNETS	
Detektor	MC2024 (Klassifizierungsdetektor)	
ÖV-Empfangsbaugruppe	Kontakte	
	FEA	
	LISA	
Sonstiges		

Verkehrsprogramme



Abkürzungen: Vollverkehrsabhängig (vva), teilverkehrsabhängig (tva), Festzeit (FZ), Umlaufzeit (tu), koordiniert (Koord.).

Nr.	Art	tu [s]	Koord.	Steuerungsart	
P1	tva	60	Ja	teilverkehrsabhängig koordiniert	
P2	tva	72	Ja	teilverkehrsabhängig koordiniert	
P3	FZ	75	Ja	Festzeit	
P4	FZ	90	Ja	Festzeit	

Historie

Datum	Autor/-in	Auftragsnummer	Änderungen
20.11.1992	Herr Antolic	??	Erstversorgung
18.06.2001	Herr Schillinger	51.5807	P1-P4 geändert; P3 und P4 Festzeit, Sy geändert
01.07.2013	VT-S/Wolz	856940075961	Neuparametrierung der Programme P3 und P4

Phasen:

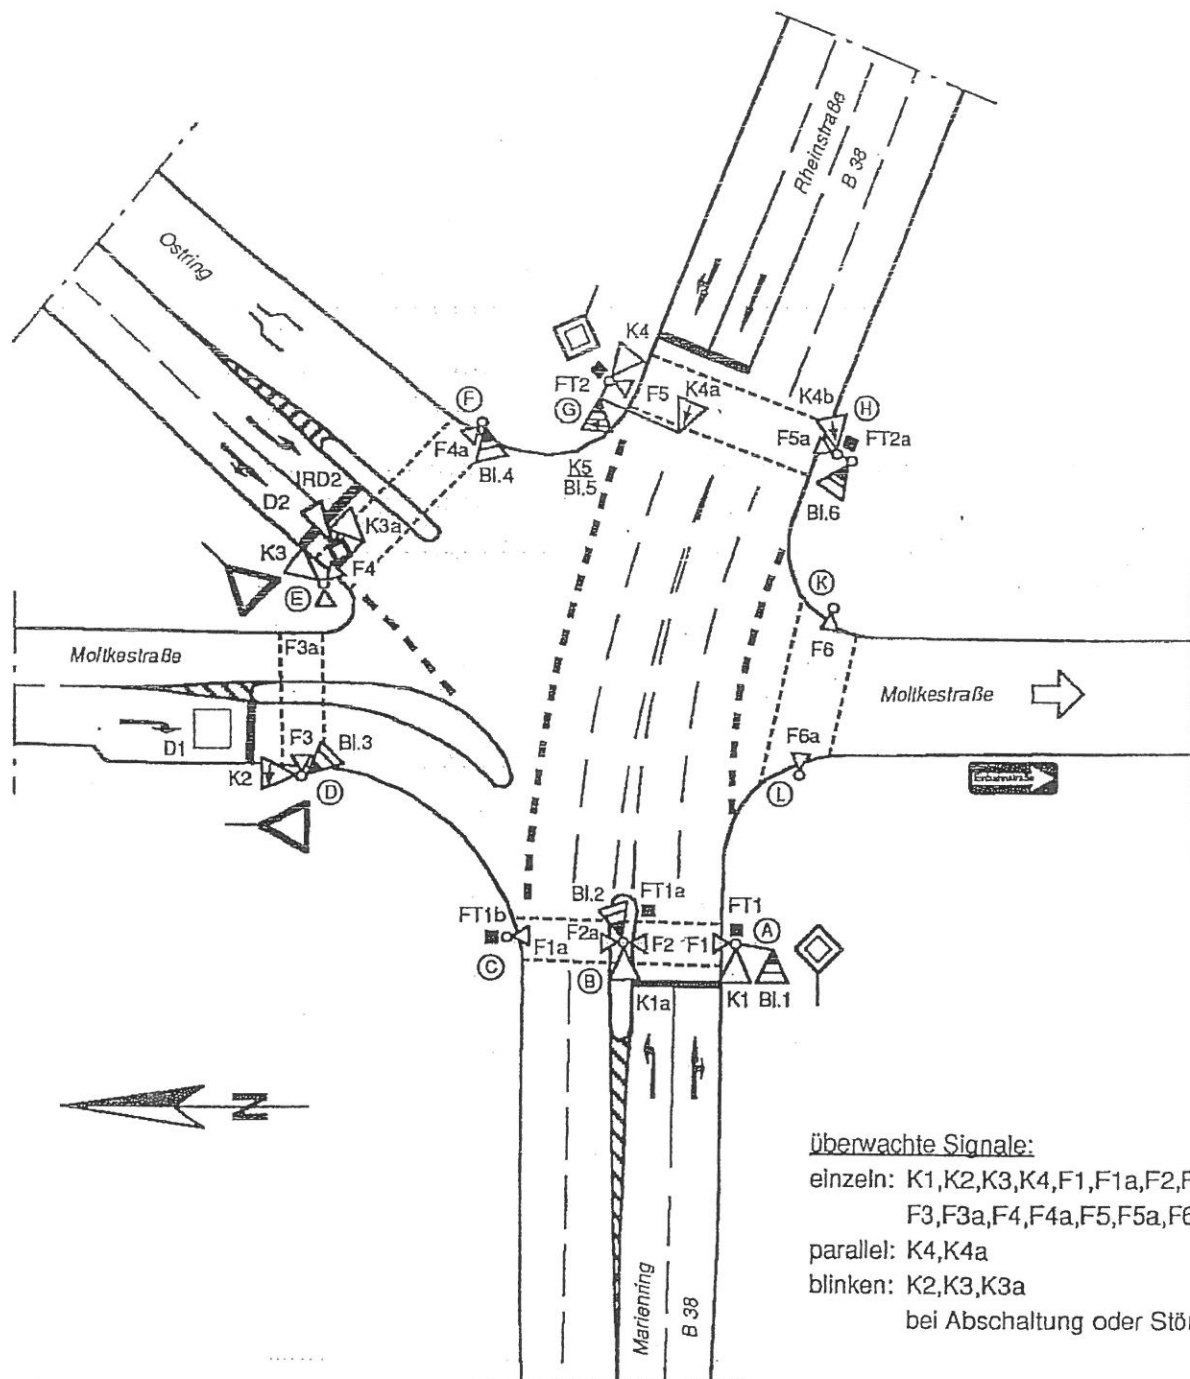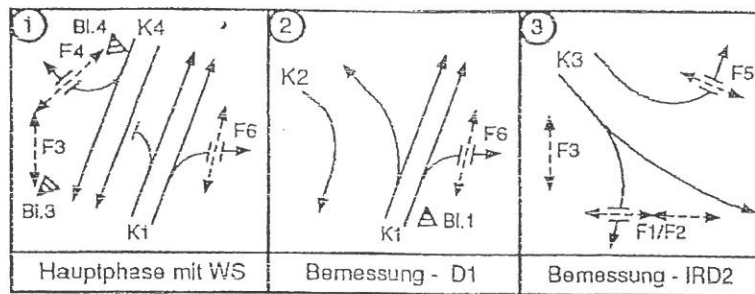

Überwachte Signale:

einzeln: K1, K2, K3, K4, F1, F1a, F2, F2a,
 F3, F3a, F4, F4a, F5, F5a, F6, F6a
 parallel: K4, K4a
 blinken: K2, K3, K3a
 bei Abschaltung oder Störung

Das Urheberrecht an dieser Zeichnung/ an diesem Entwurf gehört uns. Alle Rechte der Reproduktion und Vervielfältigung, die Verwendung von Teilen sowie jede Abänderung oder Umkonstruktion bleiben gemäß Urheberrecht ausschließlich uns vorbehalten. Die Mitteilung des Zeichnungs Inhaltes oder Zugänglichmachung oder Überlassung der Zeichnung an dritte Personen ist nicht gestattet. Die Zeichnung darf ferner ohne unsere ausdrückliche Zustimmung zu einem anderen Zweck, als sie dem Empfänger anvertraut worden ist, nicht benutzt werden. Das weiterhin bleiben alle Rechte für den Fall einer Erteilung von gewerblichen Schutzrechten jeder Art vorbehalten.

	Datum	Name		LSA	Knoten 9	Maßstab	Art
Bearb.	4.11.92	Antolc		B38 Marlenring / Am Gericht / Moltkestr.		1 : 500	Signallageplan
Gez.	16.11.92	Bechler		In LANDAU / Pfalz		Tiefbauamt	Anlage-Nr.
Gepr.	23.12.92	Antolc				Landau	ES 92 / 998

```

+-----+
| ES Nummer: 92/998                                     DAMBACH-Werke
| Ort       : Landau                                     Blatt Nr. 1
| Kreuzung  : B38(Marienring) / Am Gericht             Knoten 9
| Datum     : 28.06.2013                                Uhrzeit :13:51:29
+-----+

```

Programm Nr. 0

Nr.	T	Zuordnung	Nr.	T	Zuordnung
T 1	50		T 2	20	
T 3	0		T 4	0	
T 5	0		T 6	0	
T 7	0		T 8	0	
T 9	0		T 10	0	
T 11	3		T 12	10	
T 13	0		T 14	0	
T 15	0		T 16	0	
T 17	0		T 18	0	
T 19	0		T 20	0	
T 21	0		T 22	0	
T 23	0		T 24	0	
T 25	0		T 26	0	
T 27	0		T 28	0	
T 29	0		T 30	0	
T 31	0		T 32	0	
T 33	0		T 34	0	
T 35	0		T 36	0	
T 37	0		T 38	0	
T 39	0		T 40	1	TGB ANLAGE EIN
T 41	1	TGB ANLAGE AUS	T 42	1	TGB NETZ EIN
T 43	1	TGB HAND EIN	T 44	1	TGB HAND AUS
T 45	1	TGB DET.STOERUNG EIN	T 46	1	TGB DET.STOERUNG AUS
T 47	1	TGB TAKTFEHLER	T 48	1	TGB ZWZ-FEHLER
T 49	1	TGB VERRIEGELUNG	T 50	1	TGB ROTMELDUNG
T 51	1	TGB ROTAUSFALL	T 52	1	TGB WARTUNG EIN
T 53	1	TGB WARTUNG AUS	T 54	1	TGB AENDERUNG TZEIT
T 55	1	TGB AENDERUNG ZEITL	T 56	1	TGB PROGRAMMWECHSEL
T 57	1	TGB ALLG. STOERUNG	T 58	1	TGB MINGRUEN-FEHLER
T 59	1	TGB UMLAUFKONTROLLE	T 60	1	TGB ZWZ-KORREKTUR
T 61	1	TGB MGN-KORREKTUR	T 62	1	TGB ANWENDER 1
T 63	1	TGB ANWENDER 2	T 64	1	TGB ANWENDER 3
T 65	1	TGB ANWENDER 4	T 66	1	TGB ANWENDER 5
T 67	1		T 68	0	
T 69	0		T 70	0	
T 71	0		T 72	0	
T 73	0		T 74	0	
T 75	0		T 76	0	
T 77	0		T 78	0	
T 79	0		T 80	0	
T 81	0		T 82	0	
T 83	0		T 84	0	
T 85	0		T 86	0	
T 87	0		T 88	0	
T 89	0		T 90	0	
T 91	0		T 92	0	
T 93	0		T 94	0	
T 95	0		T 96	0	
T 97	0		T 98	0	
T 99	0		T100	0	

```

+-----+
| ES Nummer: 92/998                                     DAMBACH-Werke
| Ort       : Landau                                     Blatt Nr. 2
| Kreuzung  : B38(Marienring) / Am Gericht             Knoten 9
| Datum     : 28.06.2013                                Uhrzeit :13:51:29
+-----+

```

Programm Nr. 0

Nr.	T	Zuordnung	Nr.	T	Zuordnung
T101	0		T102	0	
T103	0		T104	0	
T105	0		T106	0	
T107	0		T108	0	
T109	0		T110	0	
T111	0		T112	0	
T113	0		T114	0	
T115	0		T116	0	
T117	0		T118	0	
T119	0		T120	0	
T121	0		T122	0	
T123	0		T124	0	
T125	0		T126	0	
T127	0		T128	0	
T129	0		T130	0	
T131	0		T132	0	
T133	0		T134	0	
T135	0		T136	0	
T137	0		T138	0	
T139	0		T140	0	
T141	0		T142	0	
T143	0		T144	0	
T145	0		T146	0	
T147	0		T148	0	
T149	0		T150	0	
T151	0		T152	0	
T153	0		T154	0	
T155	0		T156	0	
T157	0		T158	0	
T159	0		T160	0	
T161	0		T162	0	
T163	0		T164	0	
T165	0		T166	0	
T167	0		T168	0	
T169	0		T170	0	
T171	0		T172	0	
T173	0		T174	0	
T175	0		T176	0	
T177	0		T178	0	
T179	0		T180	0	
T181	0		T182	0	
T183	0		T184	0	
T185	0		T186	0	
T187	0		T188	0	
T189	0		T190	0	
T191	0		T192	0	
T193	0		T194	0	
T195	0		T196	0	
T197	0		T198	0	
T199	0		T200	0	

```

+-----+
| ES Nummer: 92/998                                     DAMBACH-Werke
| Ort       : Landau                                     Blatt Nr. 3
| Kreuzung  : B38(Marienring) / Am Gericht             Knoten 9
| Datum     : 28.06.2013                                Uhrzeit :13:51:29
+-----+

```

Programm Nr. 0

Nr.	T	Zuordnung	Nr.	T	Zuordnung
T201	0		T202	0	
T203	0		T204	0	
T205	0		T206	0	
T207	0		T208	0	
T209	0		T210	0	
T211	0		T212	0	
T213	0		T214	0	
T215	0		T216	0	
T217	0		T218	0	
T219	0		T220	0	
T221	0		T222	0	
T223	0		T224	0	
T225	0		T226	0	
T227	0		T228	0	
T229	0		T230	0	
T231	0		T232	0	
T233	0		T234	0	
T235	0		T236	0	
T237	0		T238	0	
T239	0		T240	0	
T241	0		T242	0	
T243	0		T244	0	
T245	0		T246	0	
T247	0		T248	0	
T249	0		T250	0	


```

+-----+
| ES Nummer: 92/998                                     DAMBACH-Werke
| Ort      : Landau                                     Blatt Nr. 4
| Kreuzung : B38(Marienring) / Am Gericht   Knoten 9
| Datum    : 28.06.2013                             Uhrzeit :13:51:29
+-----+

```

Programm Nr. 1

Nr.	T	Zuordnung	Nr.	T	Zuordnung
T 1	60		T 2	32	
T 3	35		T 4	1	
T 5	70		T 6	0	
T 7	0		T 8	254	
T 9	39		T 10	31	
T 11	0		T 12	0	
T 13	0		T 14	0	
T 15	0		T 16	0	
T 17	0		T 18	0	
T 19	0		T 20	0	
T 21	0		T 22	0	
T 23	0		T 24	0	
T 25	0		T 26	0	
T 27	0		T 28	0	
T 29	0		T 30	0	
T 31	0		T 32	0	
T 33	0		T 34	0	
T 35	0		T 36	0	
T 37	0		T 38	0	
T 39	0		T 40	0	
T 41	0		T 42	0	
T 43	0		T 44	0	
T 45	0		T 46	0	
T 47	0		T 48	0	
T 49	0		T 50	0	
T 51	3		T 52	30	
T 53	3		T 54	57	
T 55	22		T 56	10	
T 57	51		T 58	28	
T 59	3		T 60	55	
T 61	24		T 62	10	
T 63	17		T 64	10	
T 65	48		T 66	7	
T 67	39		T 68	26	
T 69	19		T 70	12	
T 71	3		T 72	31	
T 73	30		T 74	6	
T 75	10		T 76	29	
T 77	10		T 78	57	
T 79	30		T 80	49	
T 81	30		T 82	55	
T 83	10		T 84	29	
T 85	0		T 86	0	
T 87	0		T 88	0	
T 89	0		T 90	0	
T 91	0		T 92	0	
T 93	0		T 94	0	
T 95	0		T 96	0	
T 97	0		T 98	0	
T 99	0		T100	0	

```

+-----+
| ES Nummer: 92/998                                     DAMBACH-Werke
| Ort      : Landau                                       Blatt Nr. 5
| Kreuzung : B38(Marienring) / Am Gericht   Knoten 9
| Datum    : 28.06.2013                               Uhrzeit :13:51:29
+-----+

```

Programm Nr. 1

Nr.	T	Zuordnung	Nr.	T	Zuordnung
T101	0		T102	0	
T103	0		T104	0	
T105	0		T106	0	
T107	0		T108	0	
T109	0		T110	0	
T111	0		T112	0	
T113	0		T114	0	
T115	0		T116	0	
T117	0		T118	0	
T119	0		T120	0	
T121	0		T122	0	
T123	0		T124	0	
T125	0		T126	0	
T127	0		T128	0	
T129	0		T130	0	
T131	0		T132	0	
T133	0		T134	0	
T135	0		T136	0	
T137	0		T138	0	
T139	0		T140	0	
T141	0		T142	0	
T143	0		T144	0	
T145	0		T146	0	
T147	0		T148	0	
T149	0		T150	0	
T151	0		T152	0	
T153	0		T154	0	
T155	0		T156	0	
T157	0		T158	0	
T159	0		T160	0	
T161	0		T162	0	
T163	0		T164	0	
T165	0		T166	0	
T167	0		T168	0	
T169	0		T170	0	
T171	0		T172	0	
T173	0		T174	0	
T175	0		T176	0	
T177	0		T178	0	
T179	0		T180	0	
T181	0		T182	0	
T183	0		T184	0	
T185	0		T186	0	
T187	0		T188	0	
T189	0		T190	0	
T191	0		T192	0	
T193	0		T194	0	
T195	0		T196	0	
T197	0		T198	0	
T199	0		T200	0	

```

+-----+
| ES Nummer: 92/998                                     DAMBACH-Werke
| Ort      : Landau                                     Blatt Nr. 6
| Kreuzung : B38(Marienring) / Am Gericht   Knoten 9
| Datum    : 28.06.2013                             Uhrzeit :13:51:29
+-----+

```

Programm Nr. 1

Nr.	T	Zuordnung	Nr.	T	Zuordnung
T201	0		T202	0	
T203	0		T204	0	
T205	0		T206	0	
T207	0		T208	0	
T209	0		T210	0	
T211	0		T212	0	
T213	0		T214	0	
T215	0		T216	0	
T217	0		T218	0	
T219	0		T220	0	
T221	0		T222	0	
T223	0		T224	0	
T225	0		T226	0	
T227	0		T228	0	
T229	0		T230	0	
T231	0		T232	0	
T233	0		T234	0	
T235	0		T236	0	
T237	0		T238	0	
T239	0		T240	0	
T241	0		T242	0	
T243	0		T244	0	
T245	0		T246	0	
T247	0		T248	0	
T249	0		T250	0	

```

+-----+
| ES Nummer: 92/998                                     DAMBACH-Werke
| Ort      : Landau                                     Blatt Nr. 7
| Kreuzung : B38(Marienring) / Am Gericht             Knoten 9
| Datum    : 28.06.2013                                Uhrzeit :13:51:29
+-----+

```

Program Nr. 2

Nr.	T	Zuordnung	Nr.	T	Zuordnung
T 1	72		T 2	37	
T 3	40		T 4	1	
T 5	82		T 6	0	
T 7	0		T 8	254	
T 9	47		T 10	36	
T 11	0		T 12	0	
T 13	0		T 14	0	
T 15	0		T 16	0	
T 17	0		T 18	0	
T 19	0		T 20	0	
T 21	0		T 22	0	
T 23	0		T 24	0	
T 25	0		T 26	0	
T 27	0		T 28	0	
T 29	0		T 30	0	
T 31	0		T 32	0	
T 33	0		T 34	0	
T 35	0		T 36	0	
T 37	0		T 38	0	
T 39	0		T 40	0	
T 41	0		T 42	0	
T 43	0		T 44	0	
T 45	0		T 46	0	
T 47	0		T 48	0	
T 49	0		T 50	0	
T 51	7		T 52	35	
T 53	7		T 54	71	
T 55	27		T 56	14	
T 57	65		T 58	33	
T 59	7		T 60	69	
T 61	29		T 62	14	
T 63	22		T 64	14	
T 65	57		T 66	11	
T 67	47		T 68	31	
T 69	24		T 70	16	
T 71	7		T 72	36	
T 73	35		T 74	10	
T 75	14		T 76	34	
T 77	14		T 78	66	
T 79	35		T 80	57	
T 81	35		T 82	69	
T 83	14		T 84	34	
T 85	0		T 86	0	
T 87	0		T 88	0	
T 89	0		T 90	0	
T 91	0		T 92	0	
T 93	0		T 94	0	
T 95	0		T 96	0	
T 97	0		T 98	0	
T 99	0		T100	0	

```

+-----+
| ES Nummer: 92/998                                     DAMBACH-Werke
| Ort      : Landau                                       Blatt Nr. 8
| Kreuzung : B38(Marienring) / Am Gericht   Knoten 9
| Datum    : 28.06.2013                               Uhrzeit :13:51:29
+-----+

```

Programm Nr. 2

Nr.	T	Zuordnung	Nr.	T	Zuordnung
T101	0		T102	0	
T103	0		T104	0	
T105	0		T106	0	
T107	0		T108	0	
T109	0		T110	0	
T111	0		T112	0	
T113	0		T114	0	
T115	0		T116	0	
T117	0		T118	0	
T119	0		T120	0	
T121	0		T122	0	
T123	0		T124	0	
T125	0		T126	0	
T127	0		T128	0	
T129	0		T130	0	
T131	0		T132	0	
T133	0		T134	0	
T135	0		T136	0	
T137	0		T138	0	
T139	0		T140	0	
T141	0		T142	0	
T143	0		T144	0	
T145	0		T146	0	
T147	0		T148	0	
T149	0		T150	0	
T151	0		T152	0	
T153	0		T154	0	
T155	0		T156	0	
T157	0		T158	0	
T159	0		T160	0	
T161	0		T162	0	
T163	0		T164	0	
T165	0		T166	0	
T167	0		T168	0	
T169	0		T170	0	
T171	0		T172	0	
T173	0		T174	0	
T175	0		T176	0	
T177	0		T178	0	
T179	0		T180	0	
T181	0		T182	0	
T183	0		T184	0	
T185	0		T186	0	
T187	0		T188	0	
T189	0		T190	0	
T191	0		T192	0	
T193	0		T194	0	
T195	0		T196	0	
T197	0		T198	0	
T199	0		T200	0	

+-----+
 | ES Nummer: 92/998
 | Ort : Landau
 | Kreuzung : B38(Marienring) / Am Gericht Knoten 9
 | Datum : 28.06.2013
 +-----+

DAMBACH-Werke
 Blatt Nr. 9

Uhrzeit :13:51:29

Programm Nr. 2

Nr.	T	Zuordnung	Nr.	T	Zuordnung
T201	0		T202	0	
T203	0		T204	0	
T205	0		T206	0	
T207	0		T208	0	
T209	0		T210	0	
T211	0		T212	0	
T213	0		T214	0	
T215	0		T216	0	
T217	0		T218	0	
T219	0		T220	0	
T221	0		T222	0	
T223	0		T224	0	
T225	0		T226	0	
T227	0		T228	0	
T229	0		T230	0	
T231	0		T232	0	
T233	0		T234	0	
T235	0		T236	0	
T237	0		T238	0	
T239	0		T240	0	
T241	0		T242	0	
T243	0		T244	0	
T245	0		T246	0	
T247	0		T248	0	
T249	0		T250	0	

+-----+
 | ES Nummer: 92/998
 | Ort : Landau
 | Kreuzung : B38(Marienring) / Am Gericht Knoten 9
 | Datum : 28.06.2013
 +-----+

DAMBACH-Werke
 Blatt Nr. 10

Uhrzeit :13:51:29

Programm Nr. 3

Nr.	T	Zuordnung	Nr.	T	Zuordnung
T 1	90	Umlauf	T 2	52	Umschaltzeit
T 3	51	K-Schritt	T 4	1	Vorlauf
T 5	30	Time_Out	T 6	0	
T 7	0		T 8	254	Warteschritt
T 9	55	Start Festprogramm	T 10	50	Stop Festprogramm
T 11	254	S-Schritt	T 12	254	ZtnStartPh22 Verl.S
T 13	0		T 14	0	
T 15	0		T 16	254	Ab_B16 Ph23
T 17	10	Länge Phase_22	T 18	15	Länge Phase_23
T 19	0		T 20	0	
T 21	5	Zeit 1	T 22	7	Zeit 2
T 23	0		T 24	0	
T 25	0		T 26	254	Ab_K1 Ph22
T 27	254	Ab_K2 Ph22	T 28	254	An_K3 Ph22
T 29	254	DUE_K5 Ph22	T 30	254	An_F1 Ph22
T 31	254	An_F2 Ph22	T 32	254	An_F3 Ph22
T 33	254	An_F5 Ph22	T 34	254	AB_F6 Ph22
T 35	254	Ab_B11 Ph22	T 36	254	An_B12 Ph22
T 37	254	An_B13 Ph22	T 38	254	An_B16 Ph22
T 39	254	An_K1 Ph23	T 40	254	Ab_K3 Ph23
T 41	254	An_K4 Ph23	T 42	254	Ab_F1 Ph23
T 43	254	Ab_F2 Ph23	T 44	254	An_F4 Ph23
T 45	254	Ab_F5 Ph23	T 46	254	An_F6 Ph23
T 47	254	An_B11 Ph23	T 48	254	Ab_B12 Ph23
T 49	254	An_B14 Ph23	T 50	254	An_B15 Ph23
T 51	5	Ab_K1	T 52	45	An_K1
T 53	5	Ab_K2	T 54	87	An_K2
T 55	37	Ab_K3	T 56	12	An_K3
T 57	81	Ab_K4	T 58	43	An_K4
T 59	5	Ab_K5	T 60	85	An_K5
T 61	38	Ab_F1	T 62	12	An_F1
T 63	26	Ab_F2	T 64	12	An_F2
T 65	62	Ab_F3	T 66	9	An_F3
T 67	62	Ab_F4	T 68	42	An_F4
T 69	29	Ab_F5	T 70	14	An_F5
T 71	5	Ab_F6	T 72	46	An_F6
T 73	45	An_B11	T 74	8	Ab_B11
T 75	12	An_B12	T 76	43	Ab_B12
T 77	12	An_B13	T 78	71	Ab_B13
T 79	45	An_B14	T 80	65	Ab_B14
T 81	45	An_B15	T 82	85	Ab_B15
T 83	12	An_B16	T 84	43	Ab_B16
T 85	0		T 86	0	
T 87	0		T 88	0	
T 89	0				

+-----+
 | ES Nummer: 92/998
 | Ort : Landau DAMBACH-Werke
 | Kreuzung : B38(Marienring) / Am Gericht Blatt Nr. 11
 | Datum : 28.06.2013 Knoten 9
 +-----+ Uhrzeit :13:51:29

Programm Nr. 4

Nr.	T	Zuordnung	Nr.	T	Zuordnung
T 1	90	Umlauf	T 2	52	Umschaltzeit
T 3	51	K-Schritt	T 4	1	Vorlauf
T 5	30	Time_Out	T 6	0	
T 7	0		T 8	254	Warteschritt
T 9	53	Start Festprogramm	T 10	50	Stop Festprogramm
T 11	254	S-Schritt	T 12	254	ZtnStartPh22 Verl.S
T 13	0		T 14	0	
T 15	0		T 16	254	Ab_B16 Ph23
T 17	10	Länge Phase_22	T 18	15	Länge Phase_23
T 19	0		T 20	0	
T 21	5	Zeit 1	T 22	7	Zeit 2
T 23	0		T 24	0	
T 25	0		T 26	254	Ab_K1 Ph22
T 27	254	Ab_K2 Ph22	T 28	254	An_K3 Ph22
T 29	254	DUE_K5 Ph22	T 30	254	An_F1 Ph22
T 31	254	An_F2 Ph22	T 32	254	An_F3 Ph22
T 33	254	An_F5 Ph22	T 34	254	AB_F6 Ph22
T 35	254	Ab_B11 Ph22	T 36	254	An_B12 Ph22
T 37	254	An_B13 Ph22	T 38	254	An_B16 Ph22
T 39	254	An_K1 Ph23	T 40	254	Ab_K3 Ph23
T 41	254	An_K4 Ph23	T 42	254	Ab_F1 Ph23
T 43	254	Ab_F2 Ph23	T 44	254	An_F4 Ph23
T 45	254	Ab_F5 Ph23	T 46	254	An_F6 Ph23
T 47	254	An_B11 Ph23	T 48	254	Ab_B12 Ph23
T 49	254	An_B14 Ph23	T 50	254	An_B15 Ph23
T 51	5	Ab_K1	T 52	45	An_K1
T 53	5	Ab_K2	T 54	87	An_K2
T 55	37	Ab_K3	T 56	12	An_K3
T 57	81	Ab_K4	T 58	43	An_K4
T 59	5	Ab_K5	T 60	85	An_K5
T 61	38	Ab_F1	T 62	12	An_F1
T 63	26	Ab_F2	T 64	12	An_F2
T 65	62	Ab_F3	T 66	9	An_F3
T 67	54	Ab_F4	T 68	42	An_F4
T 69	29	Ab_F5	T 70	14	An_F5
T 71	5	Ab_F6	T 72	46	An_F6
T 73	45	An_B11	T 74	8	Ab_B11
T 75	12	An_B12	T 76	43	Ab_B12
T 77	12	An_B13	T 78	71	Ab_B13
T 79	45	An_B14	T 80	65	Ab_B14
T 81	45	An_B15	T 82	85	Ab_B15
T 83	12	An_B16	T 84	43	Ab_B16
T 85	0		T 86	0	
T 87	0		T 88	0	
T 89	0				

+-----+
 | ES Nummer: 92/998
 | Ort : Landau
 | Kreuzung : B38(Marienring) / Am Gericht Knoten 9
 | Datum : 28.06.2013
 +-----+

DAMBACH-Werke
 Blatt Nr. 12

Uhrzeit :13:51:29

Programm Nr. 5

Nr.	T	Zuordnung	Nr.	T	Zuordnung
T 1	52		T 2	5	
T 3	0		T 4	0	
T 5	0		T 6	0	
T 7	0		T 8	0	
T 9	6		T 10	1	
T 11	0		T 12	0	
T 13	0		T 14	0	
T 15	0		T 16	0	
T 17	0		T 18	0	
T 19	0		T 20	0	
T 21	0		T 22	0	
T 23	0		T 24	0	
T 25	0		T 26	0	
T 27	0		T 28	0	
T 29	0		T 30	0	
T 31	0		T 32	0	
T 33	0		T 34	0	
T 35	0		T 36	0	
T 37	0		T 38	0	
T 39	0		T 40	0	
T 41	0		T 42	0	
T 43	0		T 44	0	
T 45	0		T 46	0	
T 47	0		T 48	0	
T 49	0		T 50	0	
T 51	25		T 52	51	
T 53	25		T 54	19	
T 55	42		T 56	32	
T 57	13		T 58	51	
T 59	25		T 60	17	
T 61	41		T 62	32	
T 63	38		T 64	32	
T 65	12		T 66	29	
T 67	6		T 68	0	
T 69	42		T 70	34	
T 71	25		T 72	51	
T 73	51		T 74	28	
T 75	32		T 76	51	
T 77	32		T 78	16	
T 79	51		T 80	16	
T 81	51		T 82	17	
T 83	32		T 84	51	
T 85	0		T 86	0	
T 87	0		T 88	0	
T 89	0		T 90	0	
T 91	0		T 92	0	
T 93	0		T 94	0	
T 95	0		T 96	0	
T 97	0		T 98	0	
T 99	0		T100	0	

+-----+
| ES Nummer: 92/998

| Ort : Landau

| Kreuzung : B38(Marienring) / Am Gericht Knoten 9

| Datum : 28.06.2013

DAMBACH-Werke

Blatt Nr. 13

Uhrzeit :13:51:29
+-----+

Programm Nr. 5

Nr.	T	Zuordnung	Nr.	T	Zuordnung
T101	0		T102	0	
T103	0		T104	0	
T105	0		T106	0	
T107	0		T108	0	
T109	0		T110	0	
T111	0		T112	0	
T113	0		T114	0	
T115	0		T116	0	
T117	0		T118	0	
T119	0		T120	0	
T121	0		T122	0	
T123	0		T124	0	
T125	0		T126	0	
T127	0		T128	0	
T129	0		T130	0	
T131	0		T132	0	
T133	0		T134	0	
T135	0		T136	0	
T137	0		T138	0	
T139	0		T140	0	
T141	0		T142	0	
T143	0		T144	0	
T145	0		T146	0	
T147	0		T148	0	
T149	0		T150	0	
T151	0		T152	0	
T153	0		T154	0	
T155	0		T156	0	
T157	0		T158	0	
T159	0		T160	0	
T161	0		T162	0	
T163	0		T164	0	
T165	0		T166	0	
T167	0		T168	0	
T169	0		T170	0	
T171	0		T172	0	
T173	0		T174	0	
T175	0		T176	0	
T177	0		T178	0	
T179	0		T180	0	
T181	0		T182	0	
T183	0		T184	0	
T185	0		T186	0	
T187	0		T188	0	
T189	0		T190	0	
T191	0		T192	0	
T193	0		T194	0	
T195	0		T196	0	
T197	0		T198	0	
T199	0		T200	0	

+-----+
 | ES Nummer: 92/998
 | Ort : Landau
 | Kreuzung : B38(Marienring) / Am Gericht Knoten 9
 | Datum : 28.06.2013
 +-----+

DAMBACH-Werke
 Blatt Nr. 14

Uhrzeit :13:51:29

Programm Nr. 5

Nr.	T	Zuordnung	Nr.	T	Zuordnung
T201	0		T202	0	
T203	0		T204	0	
T205	0		T206	0	
T207	0		T208	0	
T209	0		T210	0	
T211	0		T212	0	
T213	0		T214	0	
T215	0		T216	0	
T217	0		T218	0	
T219	0		T220	0	
T221	0		T222	0	
T223	0		T224	0	
T225	0		T226	0	
T227	0		T228	0	
T229	0		T230	0	
T231	0		T232	0	
T233	0		T234	0	
T235	0		T236	0	
T237	0		T238	0	
T239	0		T240	0	
T241	0		T242	0	
T243	0		T244	0	
T245	0		T246	0	
T247	0		T248	0	
T249	0		T250	0	

+-----+
| ES Nummer: 92/998

| Ort : Landau

DAMBACH-Werke

| Kreuzung : B38(Marienring) / Am Gericht Knoten 9

Blatt Nr. 15

| Datum : 28.06.2013

Uhrzeit :13:51:29
+-----+

Programm Nr. 17

Nr.	T	Zuordnung	Nr.	T	Zuordnung
T 1	50		T 2	0	
T 3	0		T 4	0	
T 5	0		T 6	0	
T 7	0		T 8	0	
T 9	0		T 10	0	
T 11	4		T 12	0	
T 13	0		T 14	0	
T 15	0		T 16	0	
T 17	0		T 18	0	
T 19	0		T 20	0	
T 21	0		T 22	0	
T 23	0		T 24	0	
T 25	0		T 26	0	
T 27	0		T 28	0	
T 29	0		T 30	0	
T 31	0		T 32	0	
T 33	0		T 34	0	
T 35	0		T 36	0	
T 37	0		T 38	0	
T 39	0		T 40	0	
T 41	0		T 42	0	
T 43	0		T 44	0	
T 45	0		T 46	0	
T 47	0		T 48	0	
T 49	0		T 50	0	
T 51	0		T 52	0	
T 53	0		T 54	0	
T 55	0		T 56	0	
T 57	0		T 58	0	
T 59	0		T 60	0	
T 61	0		T 62	0	
T 63	0		T 64	0	
T 65	0		T 66	0	
T 67	0		T 68	0	
T 69	0		T 70	0	
T 71	0		T 72	0	
T 73	0		T 74	0	
T 75	0		T 76	0	
T 77	0		T 78	0	
T 79	0		T 80	0	
T 81	0		T 82	0	
T 83	0		T 84	0	
T 85	0		T 86	0	
T 87	0		T 88	0	
T 89	0		T 90	0	
T 91	0		T 92	0	
T 93	0		T 94	0	
T 95	0		T 96	0	
T 97	0		T 98	0	
T 99	0		T100	0	

+-----+
 | ES Nummer: 92/998
 | Ort : Landau
 | Kreuzung : B38(Marienring) / Am Gericht Knoten 9
 | Datum : 28.06.2013
 +-----+

DAMBACH-Werke
 Blatt Nr. 16
 Uhrzeit :13:51:29

Program Nr. 17

Nr.	T	Zuordnung	Nr.	T	Zuordnung
T101	0		T102	0	
T103	0		T104	0	
T105	0		T106	0	
T107	0		T108	0	
T109	0		T110	0	
T111	0		T112	0	
T113	0		T114	0	
T115	0		T116	0	
T117	0		T118	0	
T119	0		T120	0	
T121	0		T122	0	
T123	0		T124	0	
T125	0		T126	0	
T127	0		T128	0	
T129	0		T130	0	
T131	0		T132	0	
T133	0		T134	0	
T135	0		T136	0	
T137	0		T138	0	
T139	0		T140	0	
T141	0		T142	0	
T143	0		T144	0	
T145	0		T146	0	
T147	0		T148	0	
T149	0		T150	0	
T151	0		T152	0	
T153	0		T154	0	
T155	0		T156	0	
T157	0		T158	0	
T159	0		T160	0	
T161	0		T162	0	
T163	0		T164	0	
T165	0		T166	0	
T167	0		T168	0	
T169	0		T170	0	
T171	0		T172	0	
T173	0		T174	0	
T175	0		T176	0	
T177	0		T178	0	
T179	0		T180	0	
T181	0		T182	0	
T183	0		T184	0	
T185	0		T186	0	
T187	0		T188	0	
T189	0		T190	0	
T191	0		T192	0	
T193	0		T194	0	
T195	0		T196	0	
T197	0		T198	0	
T199	0		T200	0	

+-----+
 | ES Nummer: 92/998
 | Ort : Landau
 | Kreuzung : B38(Marienring) / Am Gericht Knoten 9
 | Datum : 28.06.2013
 +-----+

DAMBACH-Werke
 Blatt Nr. 17
 Uhrzeit :13:51:29

Program Nr. 17

Nr.	T	Zuordnung	Nr.	T	Zuordnung
T201	0		T202	0	
T203	0		T204	0	
T205	0		T206	0	
T207	0		T208	0	
T209	0		T210	0	
T211	0		T212	0	
T213	0		T214	0	
T215	0		T216	0	
T217	0		T218	0	
T219	0		T220	0	
T221	0		T222	0	
T223	0		T224	0	
T225	0		T226	0	
T227	0		T228	0	
T229	0		T230	0	
T231	0		T232	0	
T233	0		T234	0	
T235	0		T236	0	
T237	0		T238	0	
T239	0		T240	0	
T241	0		T242	0	
T243	0		T244	0	
T245	0		T246	0	
T247	0		T248	0	
T249	0		T250	0	